


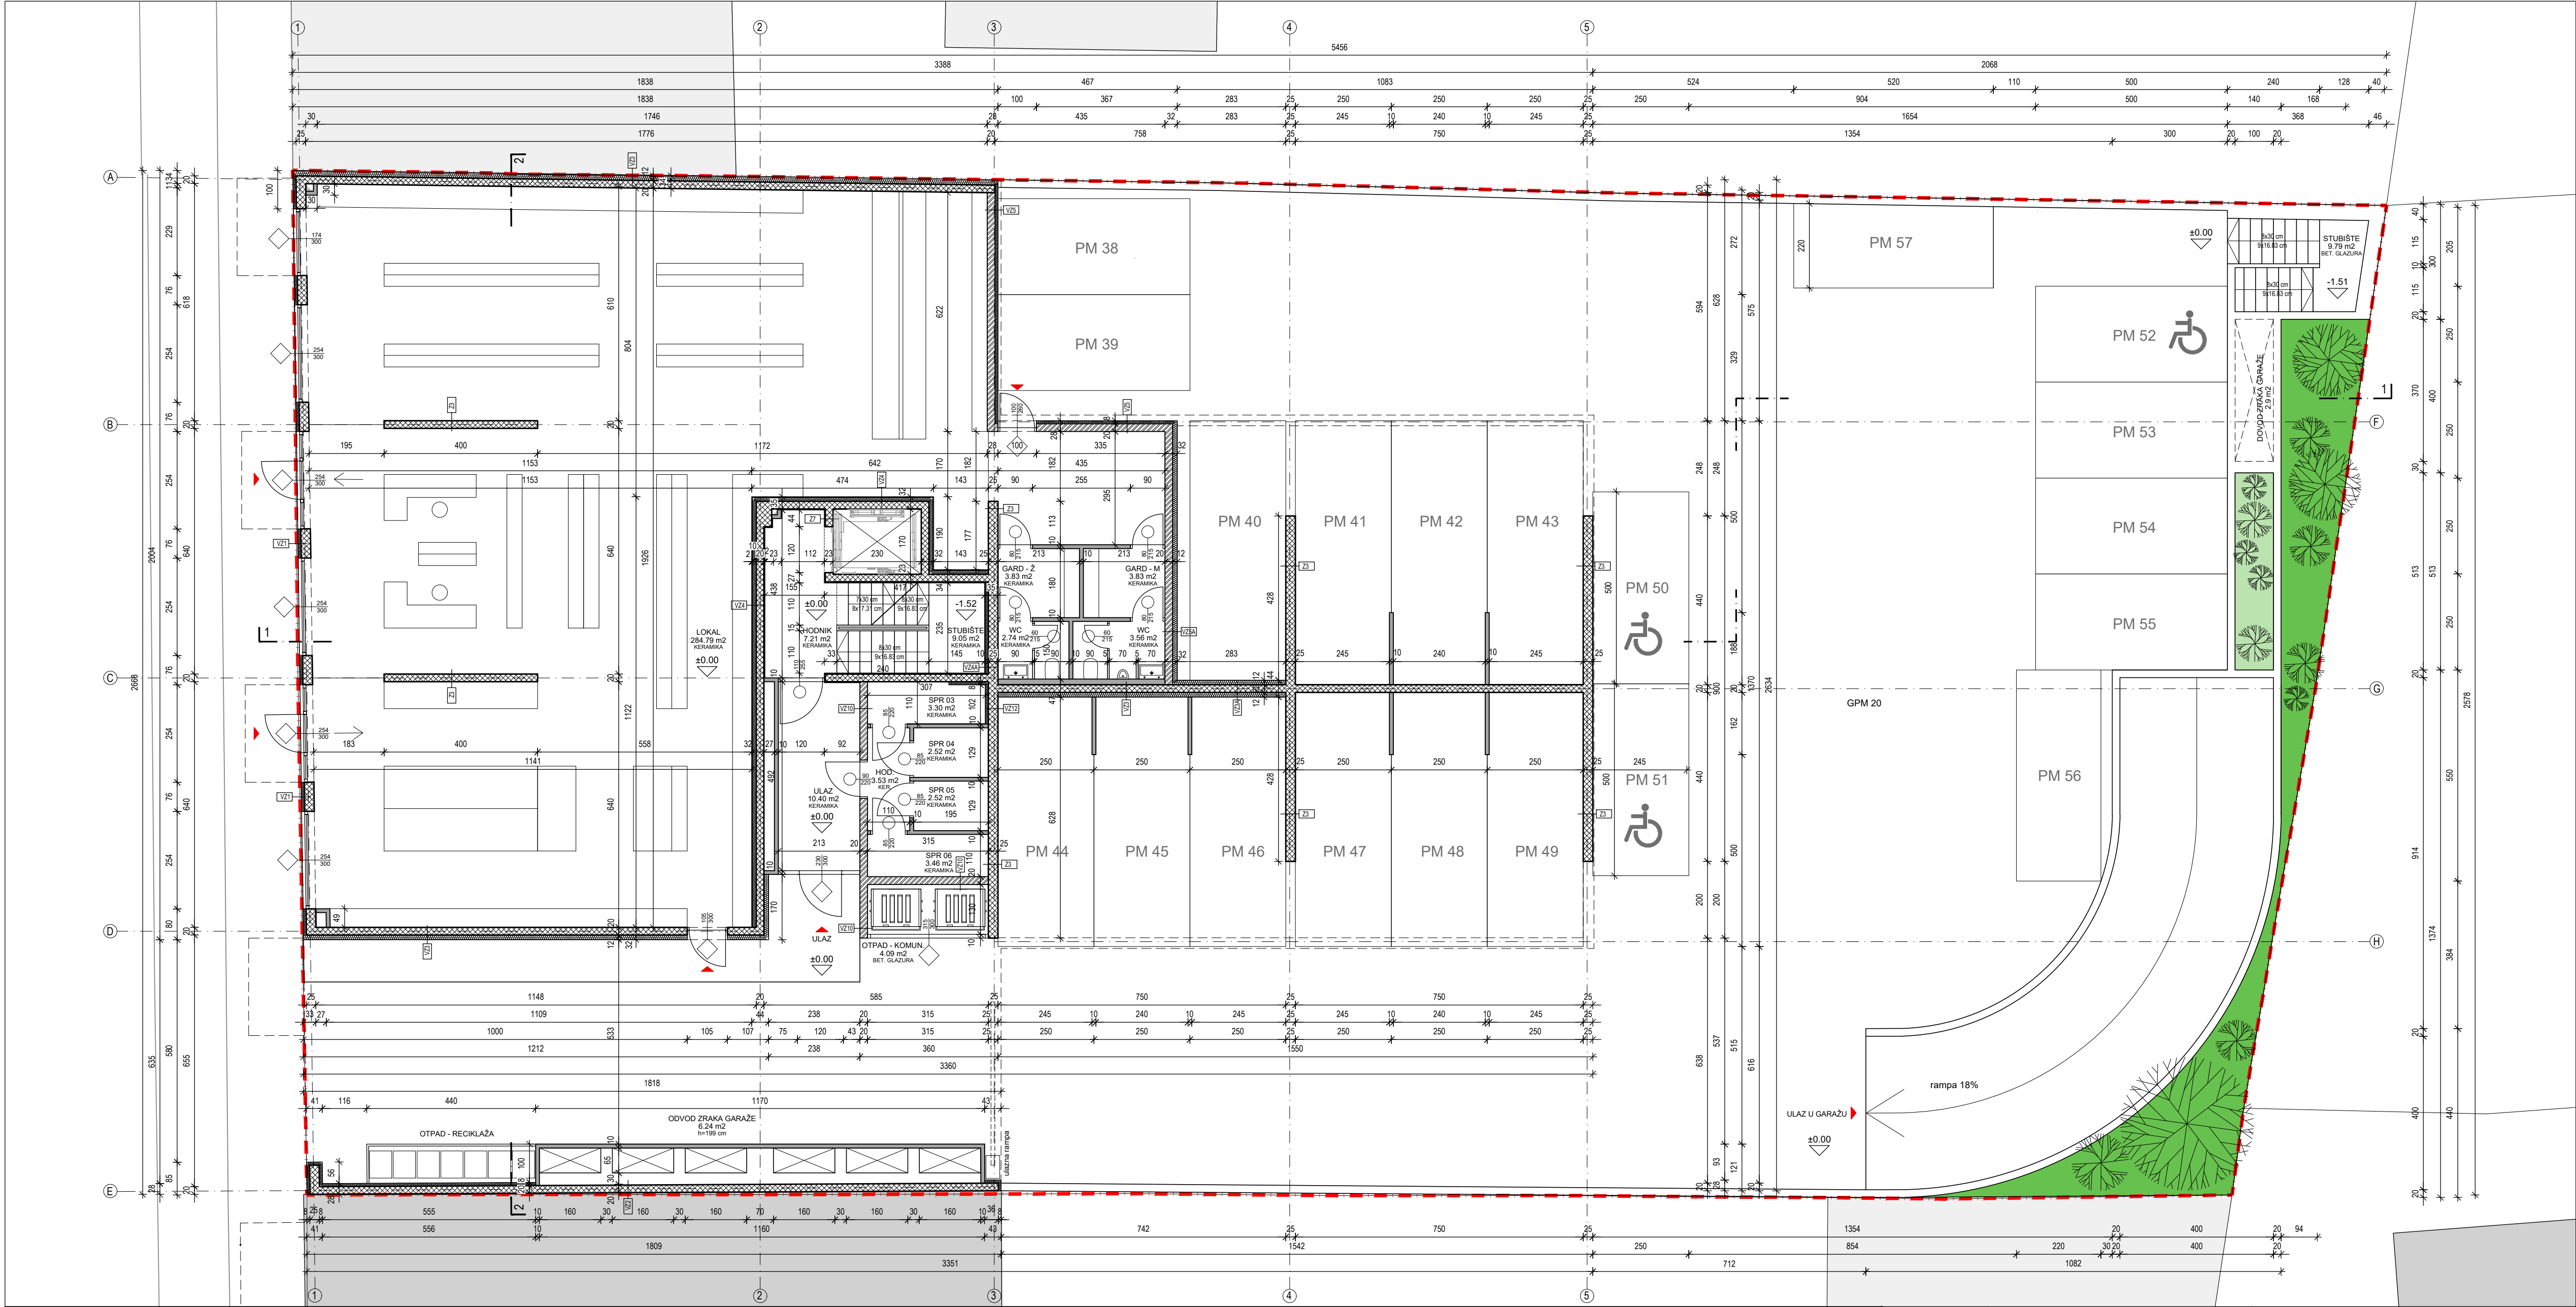

LEGENDA

- granica čestice
- oznaka presjeka
- oznaka ulaza
- svjetla širina
svjetla visina
- ◇ zidarska širina
zidarska visina
- br. širina x šir. stube
br. visina x vis. stube
- oznaka stolarije
- oznaka bravarije
- oznaka stubišta

- XXX — oznaka građevnog sloja
- p=xxx cm visina parapeta
- PROSTORIJA
m²
podna obloga oznaka prostorije

- amirani beton
- zid - zidani
- zid - gips-karton

- sloj zemlje
- prirodni teren
- ozelenjena površina

Investitor:	GWT d.o.o., Voćarska cesta 48, 10 000 Zagreb OIB: 05626170569	ARHITEKTURA SVEBOR ANDRIJEVIĆ d.o.o. Haulikova 1, HR-10 000 Zagreb	
Gradevina:	Stambeno-poslovna građevina		
Lokacija:	Nova cesta 65, na novoformiranoj čestici k.č. 1095 K.O. Trešnjevka nova, formirana spajanjem k.č. 1095 i k.č. 1096 sve K.O. Trešnjevka nova, Zagreb, Grad Zagreb		
Razina razrade:	GLAVNI PROJEKT	ZOP: 02-2024-GP	OP: 02-2024-GP-A
Vrsta projekta:	ARHITEKTONSKI PROJEKT	Mapa: 1/8	
Zahvat u prostoru:	Izgradnja nove stamb-posl.građevine umjesto postojeće	Apsolutna kota: ±0.00=+117.30 m.n.v.	
Autori:	dr.sc.Svebor Andrijević, dipl.ing.arh. Senka Dombi, dipl.ing.arh.	1	
Projektant:	dr.sc.Svebor Andrijević, dipl.ing.arh. (A4209)		
Glavni projektant:	dr.sc.Svebor Andrijević, dipl.ing.arh. (A4209)		
Projektant suradnik:	Karlo Levaj, mag.ing.arh.		
Sadržaj:	TLOCRT PRIZEMLJA	Mjerilo: 1:100 Zagreb, siječanj 2025.	Revizija: 00 List: 3.2.3.